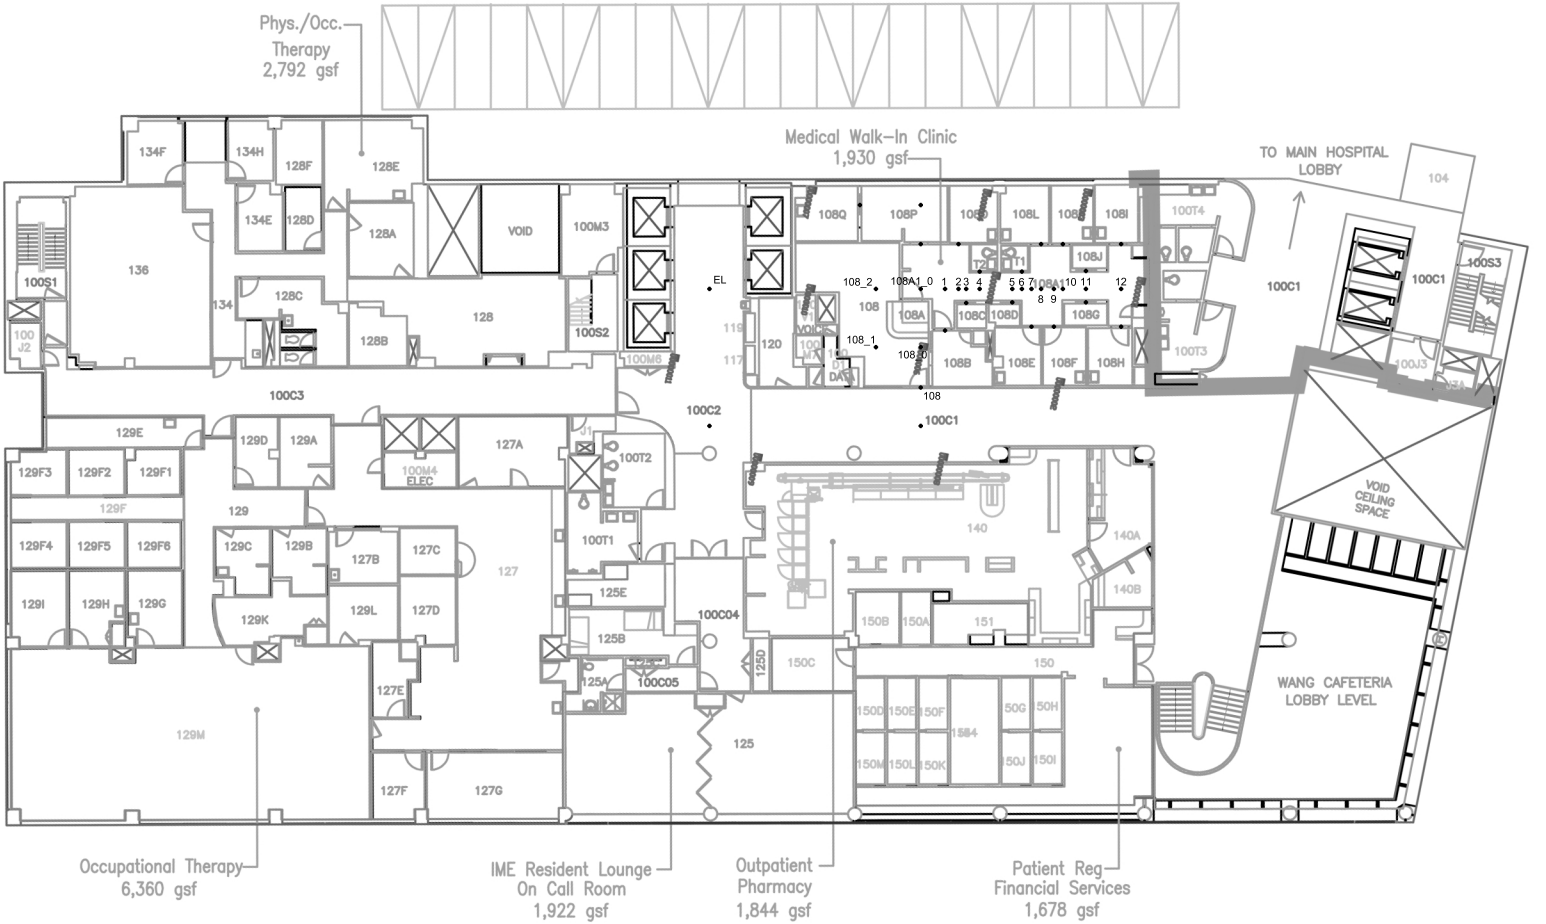
Phys./Occ. Therapy 2,792 gsf
Medical Walk-In Clinic 1,930 gsf
TO MAIN HOSPITAL LOBBY
VOID CEILING SPACE
WANG CAFETERIA LOBBY LEVEL
Occupational Therapy 6,360 gsf
IME Resident Lounge On Call Room 1,922 gsf
Outpatient Pharmacy 1,844 gsf
Patient Reg Financial Services 1,678 gsf